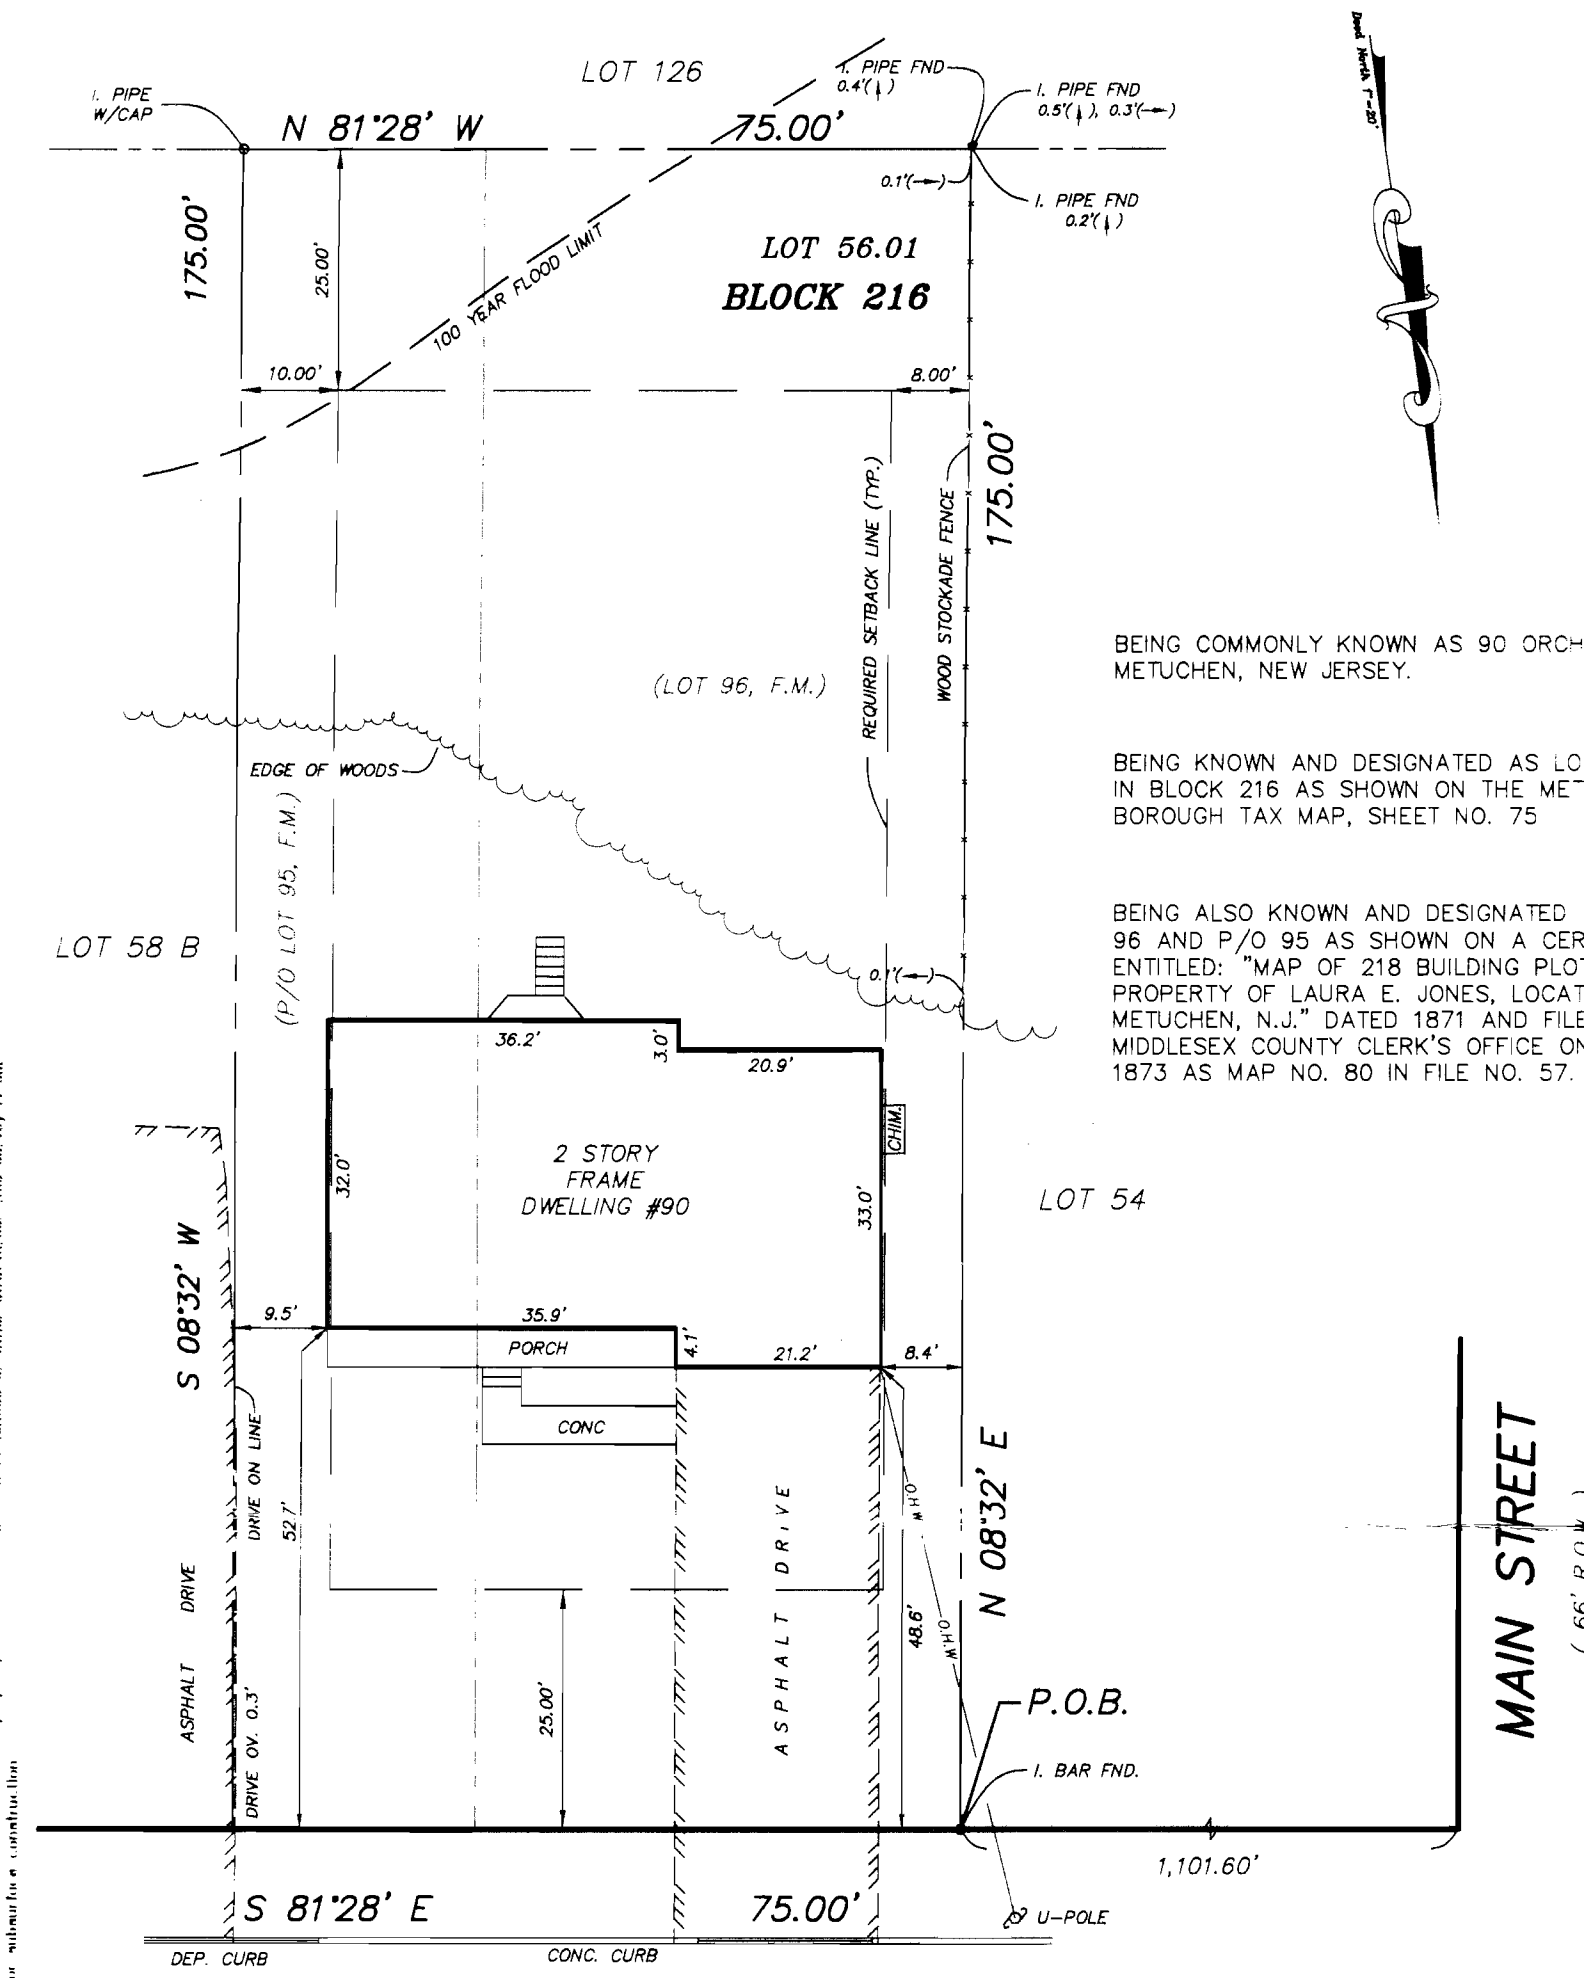

BEING COMMONLY KNOWN AS 90 ORCH
METUCHEN, NEW JERSEY.

BEING KNOWN AND DESIGNATED AS LO
IN BLOCK 216 AS SHOWN ON THE MET
BOROUGH TAX MAP, SHEET NO. 75

BEING ALSO KNOWN AND DESIGNATED
96 AND P/O 95 AS SHOWN ON A CER
ENTITLED: "MAP OF 218 BUILDING PLOT
PROPERTY OF LAURA E. JONES, LOCAT
METUCHEN, N.J." DATED 1871 AND FILE
MIDDLESEX COUNTY CLERK'S OFFICE ON
1873 AS MAP NO. 80 IN FILE NO. 57.